



1 Dito 3 - Planimetria di tracciamento pali
1 : 100

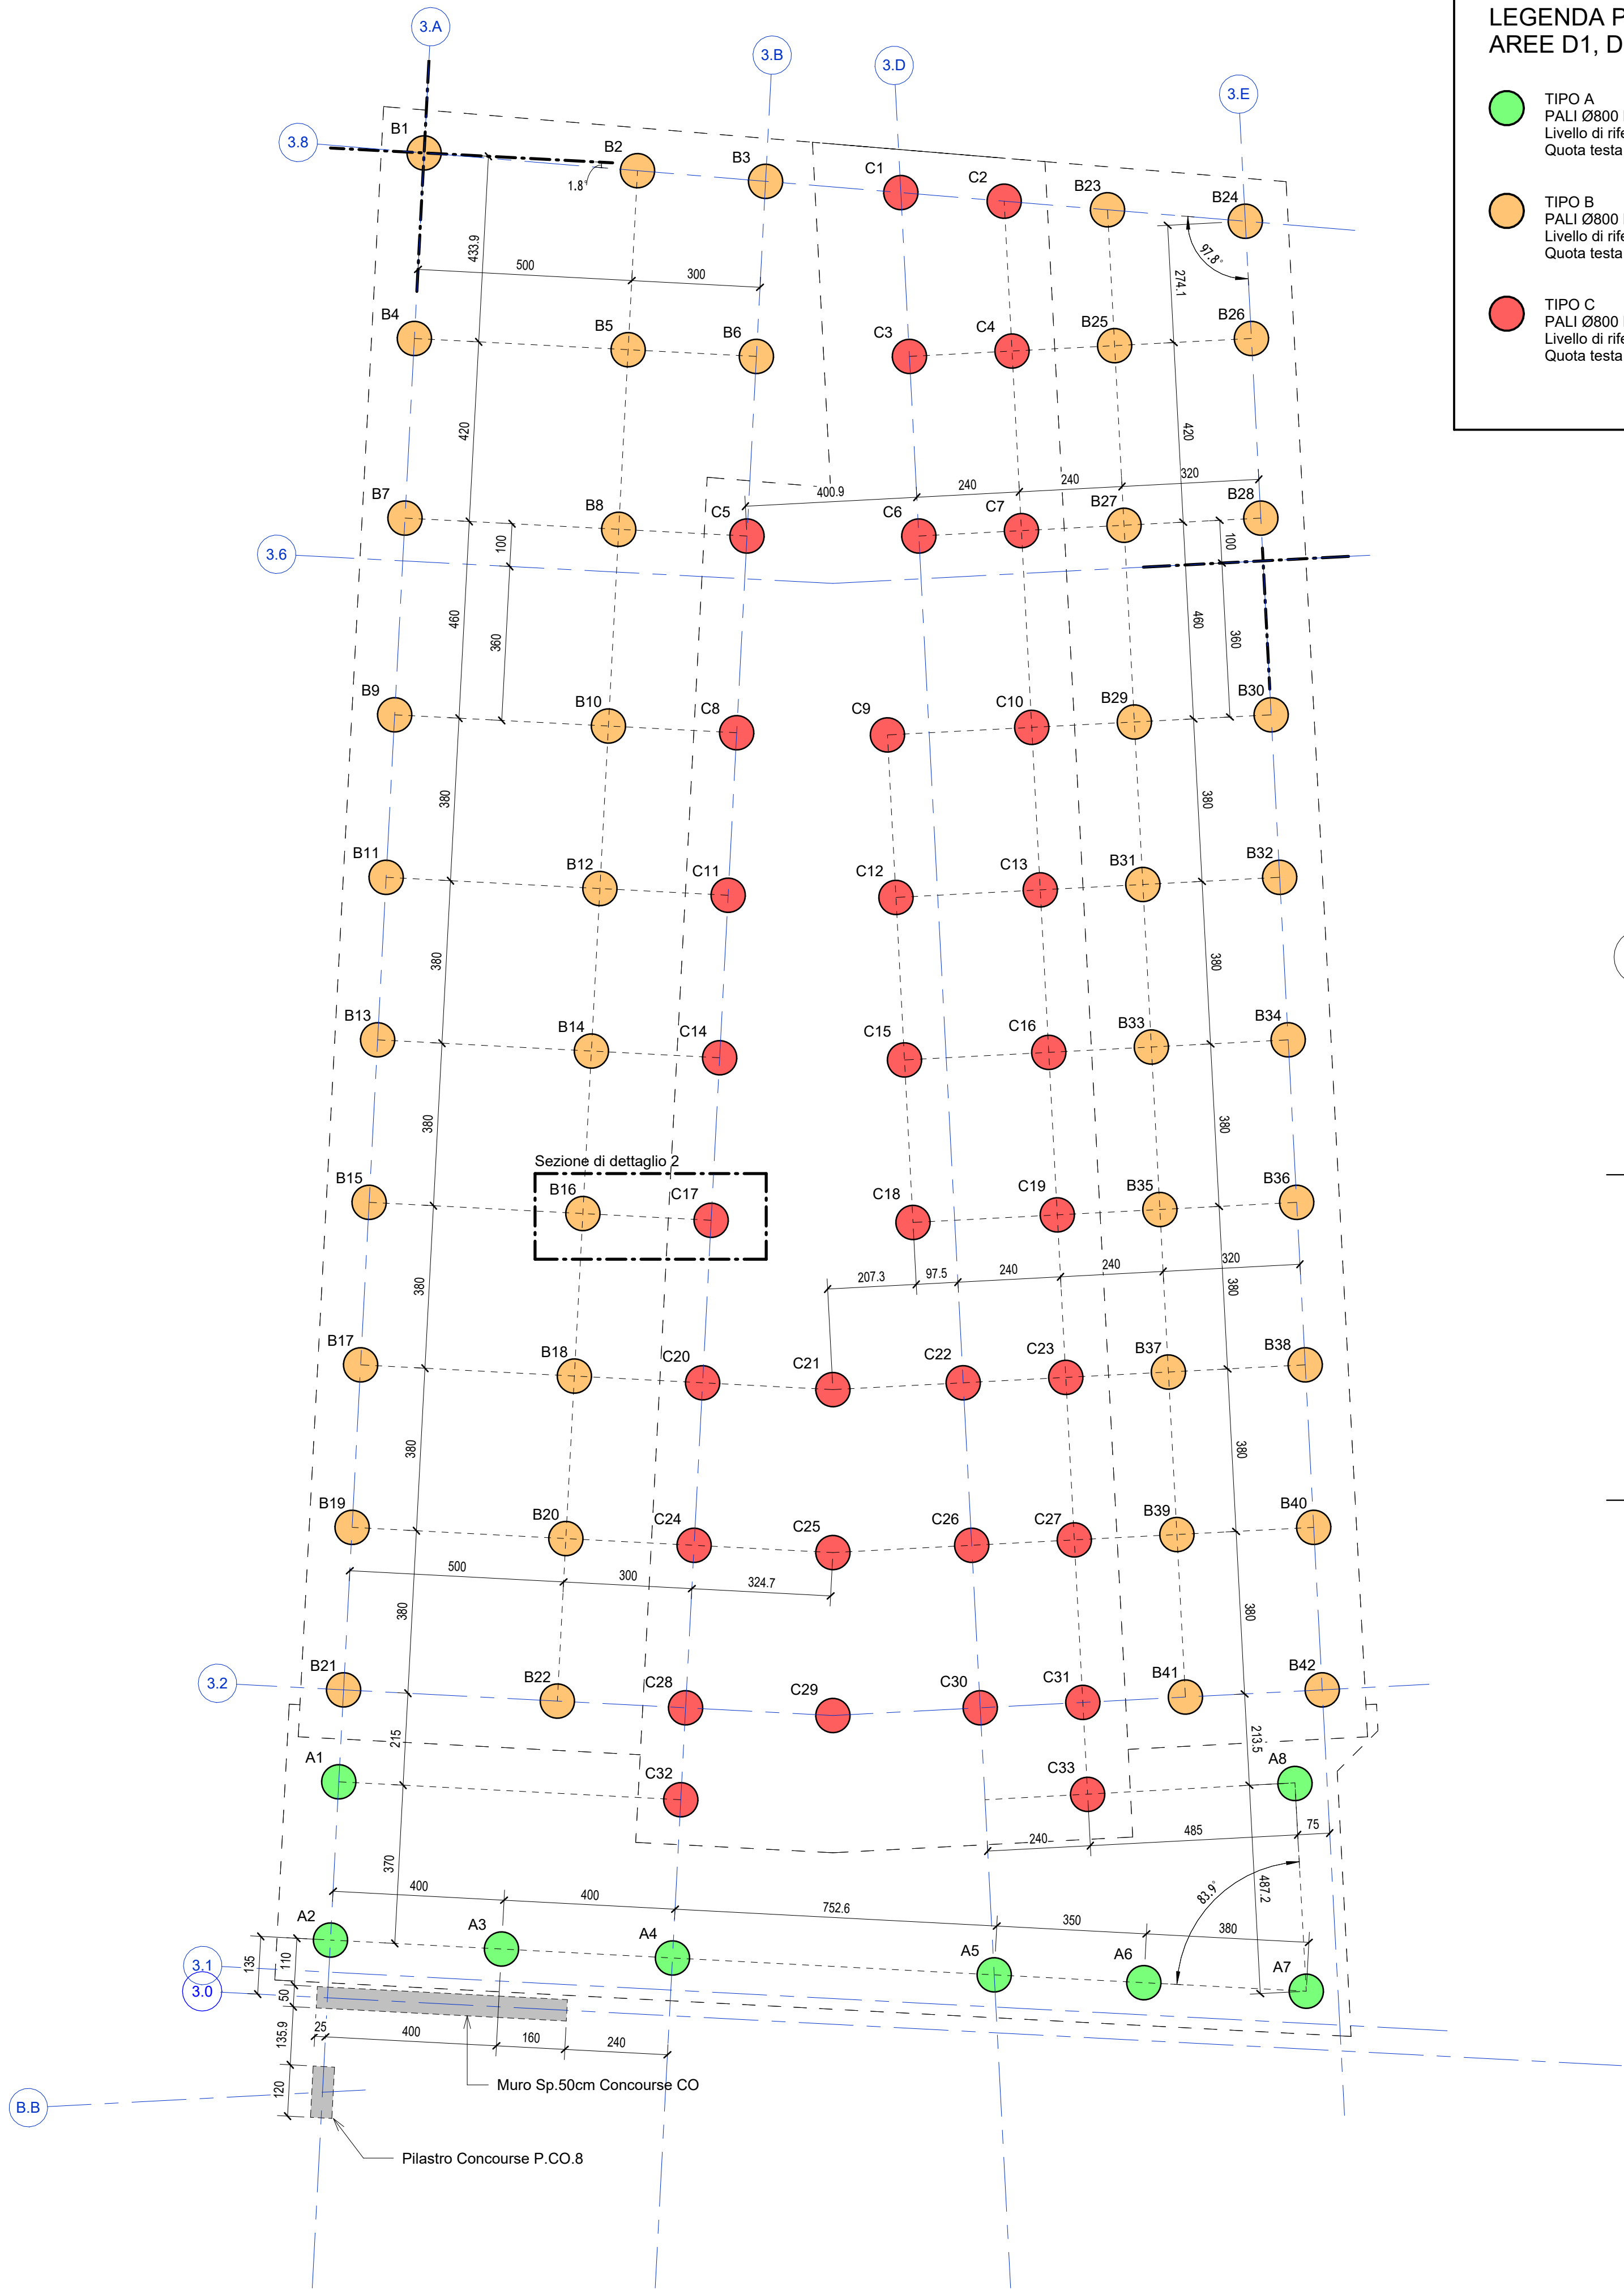


- LEGENDA PALI
AREE D1, D2, D3**
- TIPO A
PALI Ø800 L=16.0m
Livello di riferimento RF11
Quota testa palo (-6.15 m)
 - TIPO B
PALI Ø800 L=16.0m
Livello di riferimento RF12
Quota testa palo (-11.15 m)
 - TIPO C
PALI Ø800 L=16.0m
Livello di riferimento RF13
Quota testa palo (-14.95 m)

2 Sezione di dettaglio palo
1 : 50

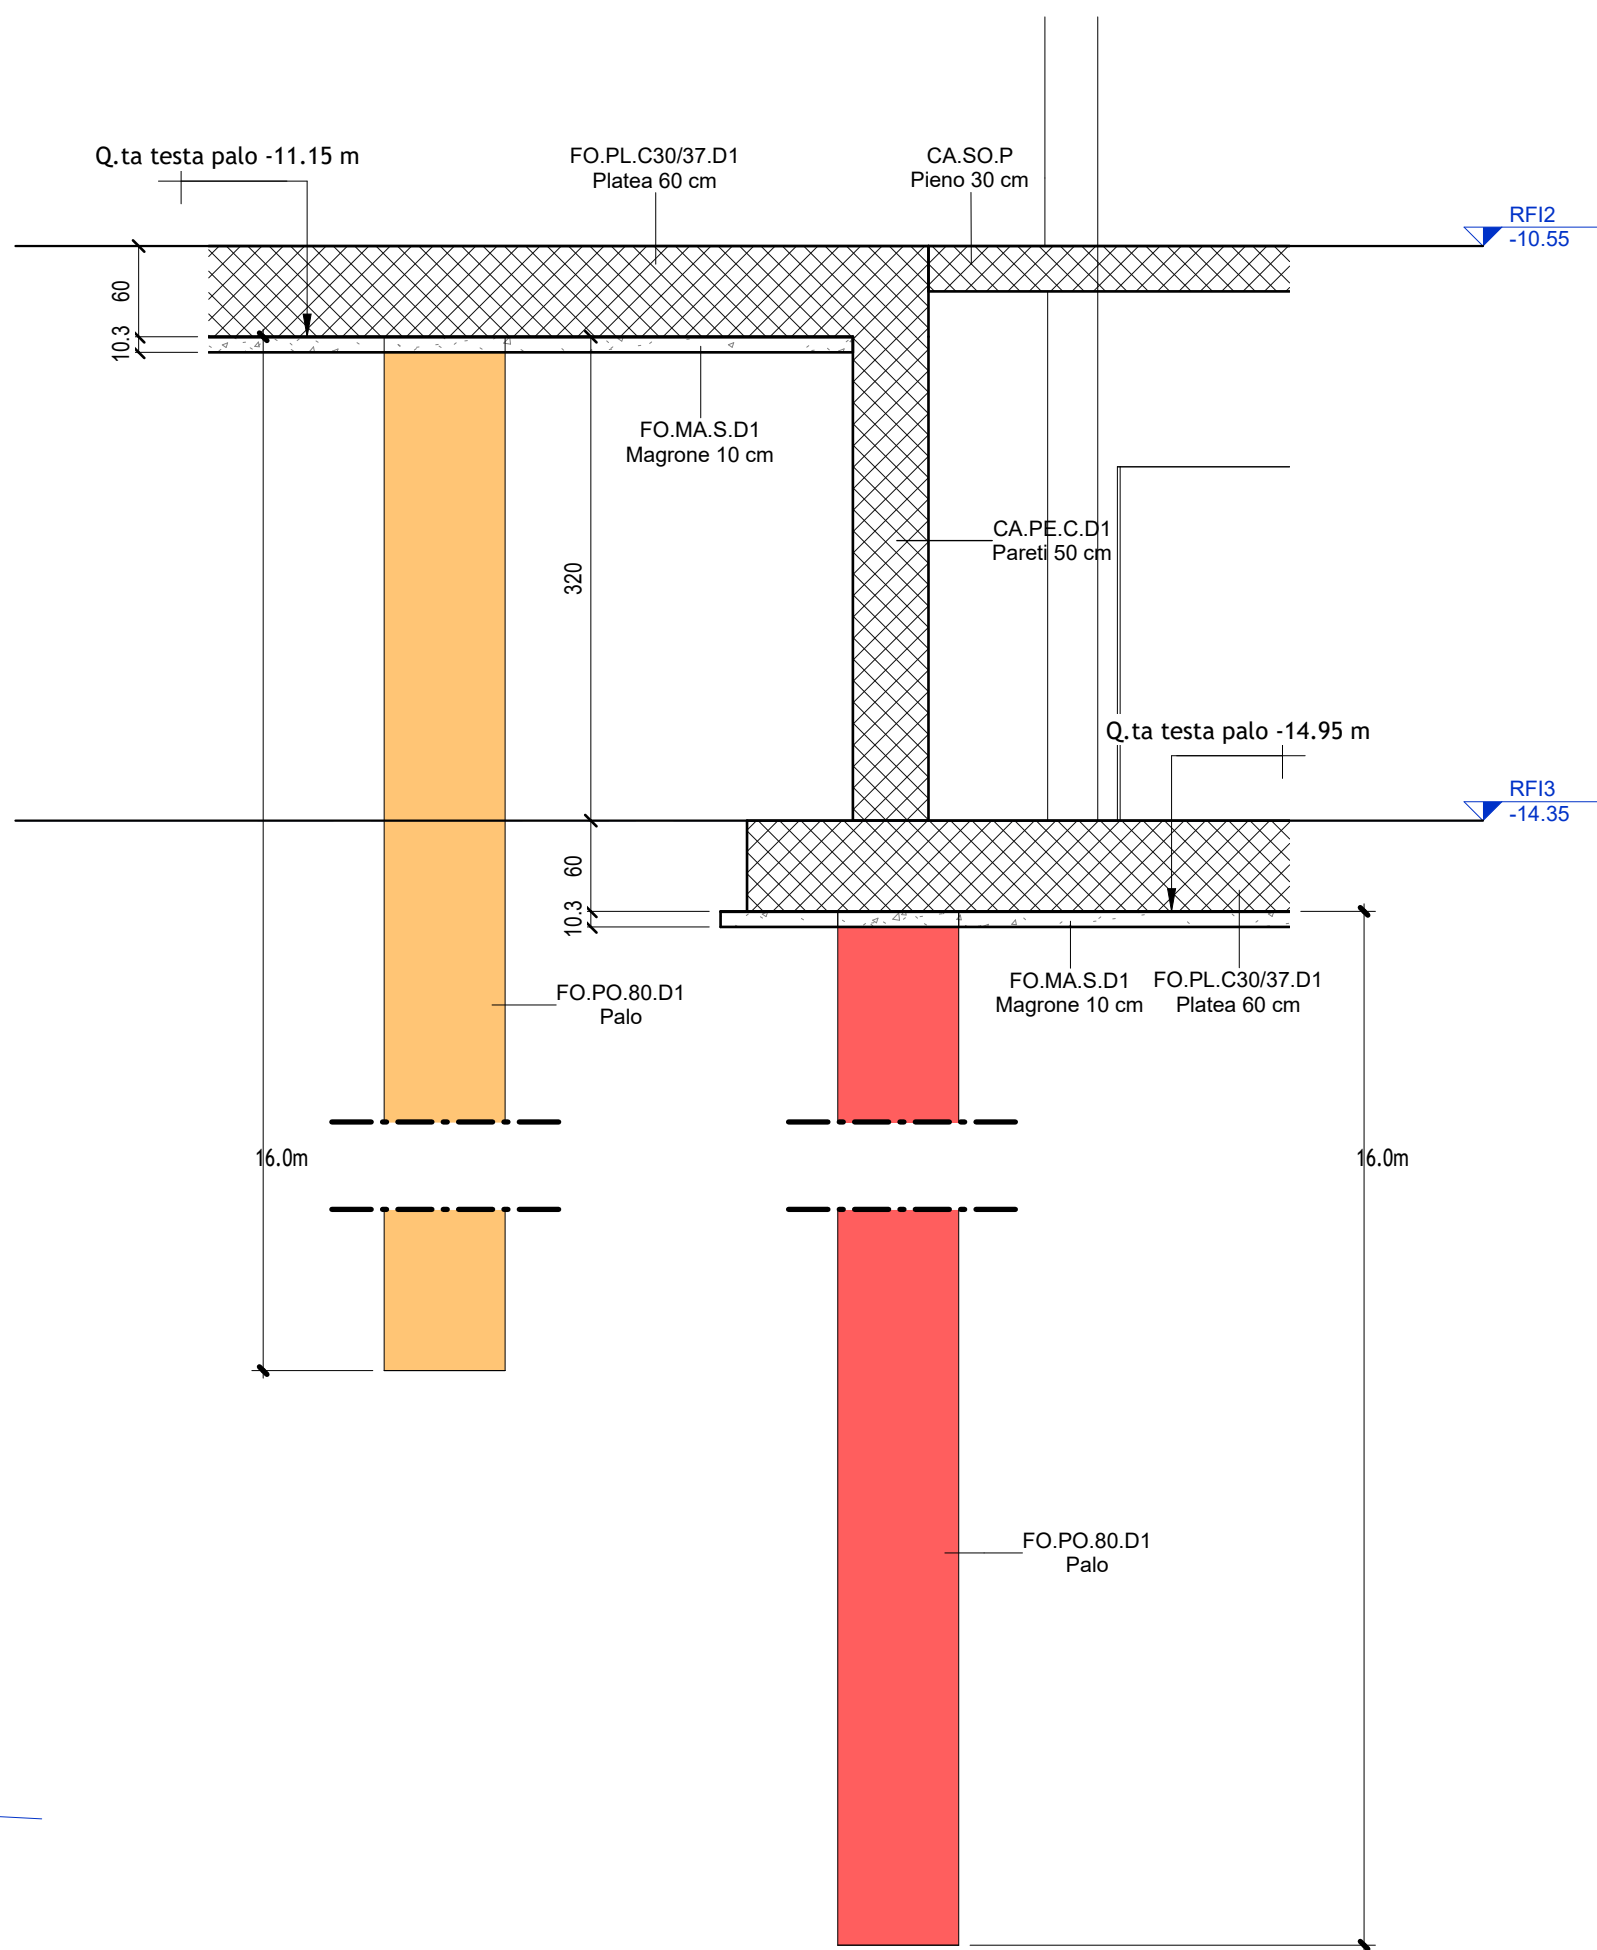

Keyplan Livelli

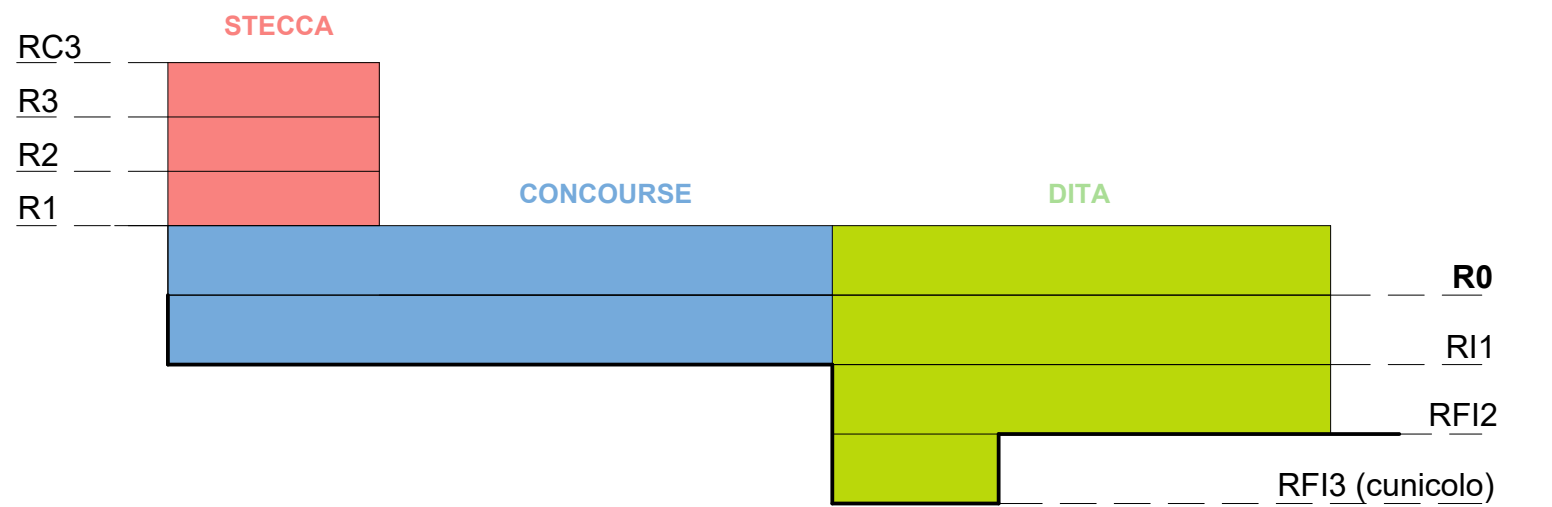

LIVELLI		
NOME	QUOTA RELATIVA	QUOTA ASSOLUTA
RC3	20.25 m	369.84 m
R3	16.95 m	366.54 m
RT	14.45 m	364.04 m
R2	11.32 m	360.91 m
RC1.2	7.64 m	357.23 m
R1	5.60 m	355.19 m
RC1.1	4.70 m	354.29 m
R0	-0.05 m	349.54 m
RF0	-0.55 m	349.04 m
RI1	-5.10 m	344.49 m
RF11.1	-5.55 m	344.04 m
RF11.2	-8.05 m	341.54 m
RFI2	-10.55 m	339.04 m
RFI3	-14.35 m	335.24 m

TABELLA MATERIALI

CALCESTRUZZO		ACCIAIO PER C.A.	
PALI	CLASSE C25/30 Classe di consistenza S5 Classe di esposizione XC2 Copriferro 4.0 cm	BARRE	CLASSE B450C $f_{yk} \geq 450$ MPa $f_{tk} \geq 540$ MPa All. ≥ 7.5 %
FONDAZIONI	CLASSE C30/37 Classe di consistenza S5 Classe di esposizione XC2 Copriferro 4.5 cm	R.E.S.	CLASSE B450A $f_{yk} \geq 450$ MPa $f_{tk} \geq 540$ MPa All. ≥ 2.5 %
ELEVAZIONE (Pilastri e pareti)	CLASSE C35/45 Classe di consistenza S4 Classe di esposizione XC1 Pilastri 4.5 cm Muri controterra 3.5 cm Pareti e solette 2.5 cm		
Copriferri:			
SOLAI COBIAX	CLASSE C30/37 Classe di consistenza S5 Classe di esposizione XC1 Copriferro 3.0 cm armatura corrente (min.2.5 cm)		

COMMITTENTE

IZS'
TERAMO

ISTITUTO ZOOPROFILATTICO SPERIMENTALE DELL'ABRUZZO E DEL MOLISE "G. CAPORALE"

PROGETTAZIONE PER LA COSTRUZIONE DELLA NUOVA SEDE DELL'IZSAM

Aggiornamento del progetto definitivo ed elaborazione della progettazione esecutiva per la Nuova sede dell'Istituto Zooprofilattico Sperimentale dell'Abruzzo e del Molise "G. Caporale" in Teramo, località Colleaterrato Alto

Addendum convenzione per l'incarico di progettazione per la costruzione della nuova sede dell'Istituto Zooprofilattico Sperimentale dell'Abruzzo e del Molise "G. Caporale" di Teramo, Rep.n.203, registrata all'Agenzia delle Entrate di Roma il 04/08/2022 al n. 3841 Serie III. In riferimento alla "convenzione per l'incarico di progettazione per la costruzione della nuova sede dell'Istituto Zooprofilattico Sperimentale "G. Caporale" di Teramo", Rep. n. 158, registrata all'Agenzia delle Entrate di Teramo il 19/05/2005 al n. 1319 Serie III A. CUP: B49D 17018680005 - CIG: 90849530A6

OPERATORE ECONOMICO

SPAINI
SPAINI ARCHITETTI ASSOCIATI S.R.L.
Via Guido D'Arezzo 16 00198 Roma
www.spainiia.com

OPERATORE ECONOMICO AUSILIARIO

ENGEKO S.C.A.R.L.
Via Guido D'Arezzo 16 00198 Roma
www.engeko.com

SEQUAS Ingegneria s.r.l. SOCIETA' BENEFIT
Via Cossaria 2 00192 Roma

SETIN SERVIZI TECNICI INFRASTRUTTURE S.R.L.
Via Guido D'Arezzo 16 00198 Roma

PROGETTISTI

COORDINAMENTO E ARCHITETTURA
Arch. Filippo Spaini

IMPIANTI
Ing. Saverio Andreani

STRUTTURE
Ing. Filippo Daniele

PROGETTO ESECUTIVO

Dito 3 - Planimetria di tracciamento pali

NOME ELABORATO

IZS_AM-PE-L2-D-ED-ST-D3-01_01

CODICE ELABORATO :

SCALA :

Come indicato

REVISIONE	DATA EMISSIONE	DESCRIZIONE	REDATTO
00	21/06/2025	Emissione	SETIN
01	28/11/2025	Revisione	SETIN